

MLTX-02-005-PRO-TS9-1-LS-SDW-0005-01

Asphalt layer for football playground

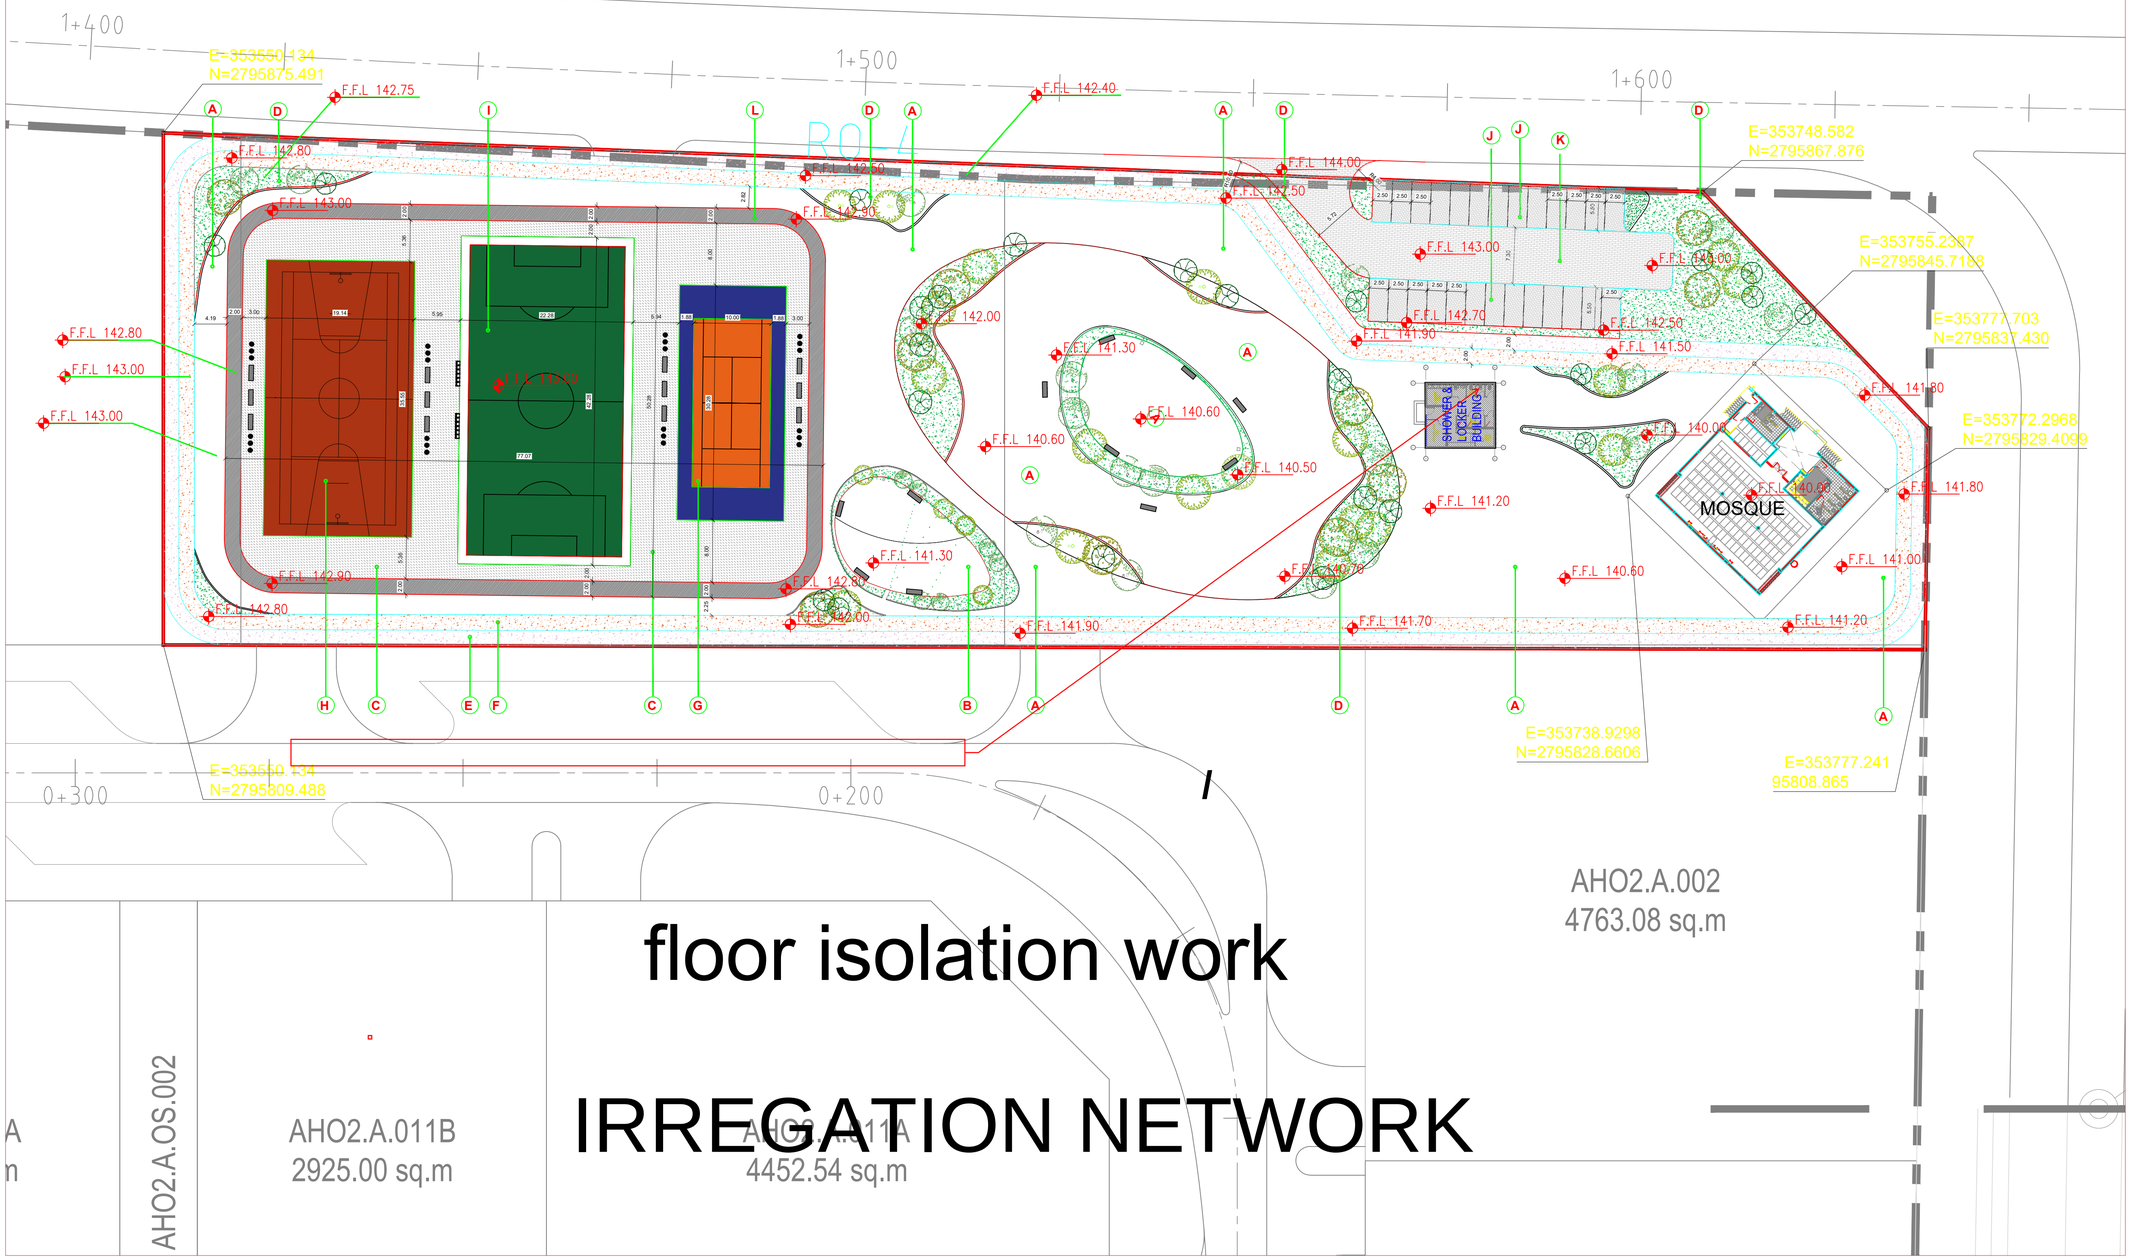

KEY PLAN :

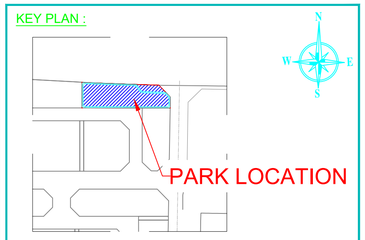

NOTES :

LEGEND :

PARK BOUNDARY
SCOPE OF WORK

- A GROUND NATURAL SOIL
- B TARTAN AREAS FOR SPORT OR PLAY GROUND AREAS
- C INTERLOCK TILES GREY SCALE WITH BLACK MARBLE CHIPS 600X300X60 MM ZERO JOINT
- D GRASS COVER .
- E BIKE PATH (BLUE COLOR)
- F WALKING PATH (RED COLOR)
- G PEDAL PLAYGROUND AS PER DETAIL
- H BASKET BALL L PLAYGROUND AS PER DETAIL
- I FOOTBALL PLAYGROUND AS PER DETAIL
- J TYPE 1 - INTERLOCK TILES 8 CM FOR PARKING
- K TYPE 2 - INTERLOCK TILES 8 CM FOR PARKING
- L STAMPED CONCRETE AS PER APPROVAL

REFRENCE TO DRAWING NUMBER:
HSA3-01-021-DAR-ST8-0-LS-DWG-1000-00

REV.No	DATE	DESCRIPTION	DRAWN	CHECKED
01	14\4\2026	LAYOUT PLAN AND LEVELS	A.A	M.S

CLIENT: MODON مدن — الهيئة السعودية للمدن الصناعية ومناطق التقنية — Saudi Authority for Industrial Cities and Technology Zones

DESIGNER : DAR AL RIYADH دار الرياض
PO Box 5364 Riyadh 11422 KSA - T: +966 11 4641611 F: +966 11 4648853

CONSULTANT : egis

CONTRACTOR : PROFAST
P.O. Box 104081 - Riyadh 11626 , SA T:+966114914810 F:+966114913380

PROJECT NAME :
PLAYGROUNDS INTITATIVE
(ALHASA-ARAR-DAMMAM)

DISCIPLINE :
LANDSCAPE ALHASA

DRAWING TITLE :
LAYOUT PLAN AND LEVELS

DRAWING NO :
MLTX-02-005-PRO-TS9-1-LS-SDW-0005-01


DRAWN BY:	CHECKED:	APPROVED BY:	REVISION:
A.A	M.S	M.N	01

DESCRIPTION :	SCALE :	DATE :
SHOP DRAWING	N.T.S	14/04/2026

Original Drawing Size A1

Pouring ofslab on grade for padel & basket playground

Duct installation

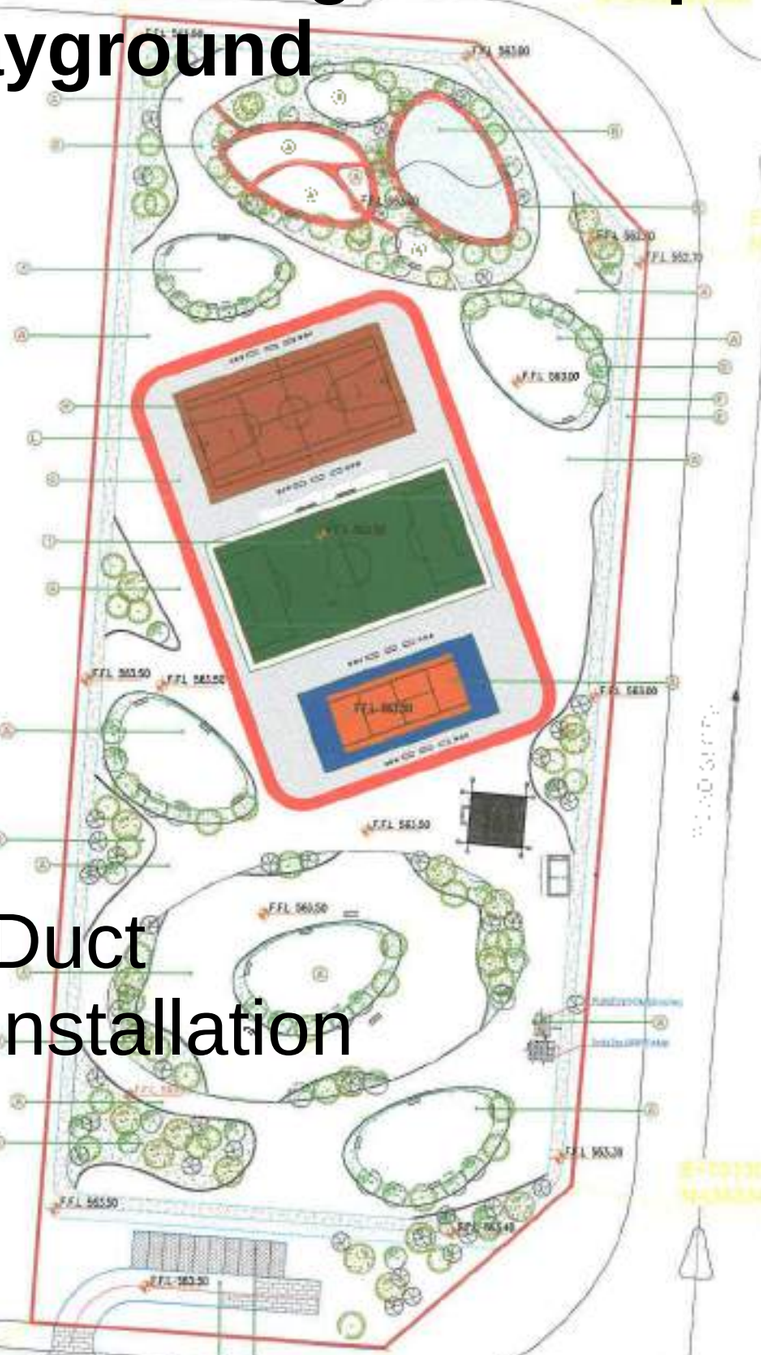

MLTX-02-005-PRO-TS9-1-LS-SDW-0005-00

Pouring ofslab on grade for padel & basket playground

Pouring of air dome foundation

Roof isolation

E=397370.618
N=2901405.980

E=397309.883
N=2901376.505

E=397296.668
N=2901369.284

E=397412.638
N=2901334.875

E=397354.159
N=2901301.534

-22.90
-22.90
Existing Walkway level
-22.90
-22.60
-22.90
-22.60
-22.90
-22.60
-22.90
-22.60
-22.90
Existing Walkway
Existing Walkway
AREA 175
SHOWER & LOCKER BUILDING

KEY PLAN :

PARK LOCATION

NOTES :

LEGEND :

PARK BOUNDARY SCOPE OF WORK

- A GROUND NATURAL SOIL
- B TARTAN AREAS FOR SPORT OR PLAY GROUND AREAS
- C INTERLOCK TILES GREY SCALE WITH BLACK MARBLE CHIPS 600X300X60 MM ZERO JOINT
- D GRASS COVER .
- E BIKE PATH (BLUE COLOR)
- F WALKING PATH (RED COLOR)
- G PEDAL PLAYGROUND AS PER DETAIL
- H BASKET BALL L PLAYGROUND AS PER DETAIL
- I FOOTBALL PLAYGROUND AS PER DETAIL
- J TYPE 1 - INTERLOCK TILES 8 CM FOR PARKING
- K TYPE 2 - INTERLOCK TILES 8 CM FOR PARKING
- L STAMPED CONCRETE AS PER APPROVAL

REFRENCE TO DRAWING NUMBER:
DAM2-01-034-PRO-ST8-0-LS-DWG-1000-00

REV.No	DATE	DESCRIPTION	DRAWN	CHECKED

CLIENT: MODON

DESIGNER : DAR AL RIYADH
PO Box 5364 Riyadh 11422 KSA - T: +966 11 4641611 F: +966 11 4648853

CONSULTANT : egis

CONTRACTOR : PROFAST
P.O. Box 104081 - Riyadh 11626 , SA T:+966114914810 F:+966114913380

PROJECT NAME :
PLAYGROUNDS INTITATIVE
(ALHASA-ARAR-DAMMAM)

DISCIPLINE :
LANDSCAPE DAMMAM

DRAWING TITLE :
LAYOUT PLAN AND LEVELS

DRAWING NO :
MLTX-02-005-PRO-TS9-1-LS-SDW-0004-00

DRAWN BY:	CHECKED:	APPROVED BY:	REVISION:
A.A	M.S	M.N	00

DESCRIPTION :	SCALE :	DATE :
FEED PACKAGE	N.T.S	07/04/2026

Original Drawing Size A1